
Bachelor Degree Project in Architecture

First cycle, 15.0 hp

Nya Elverket

NILS WALDEMARSON

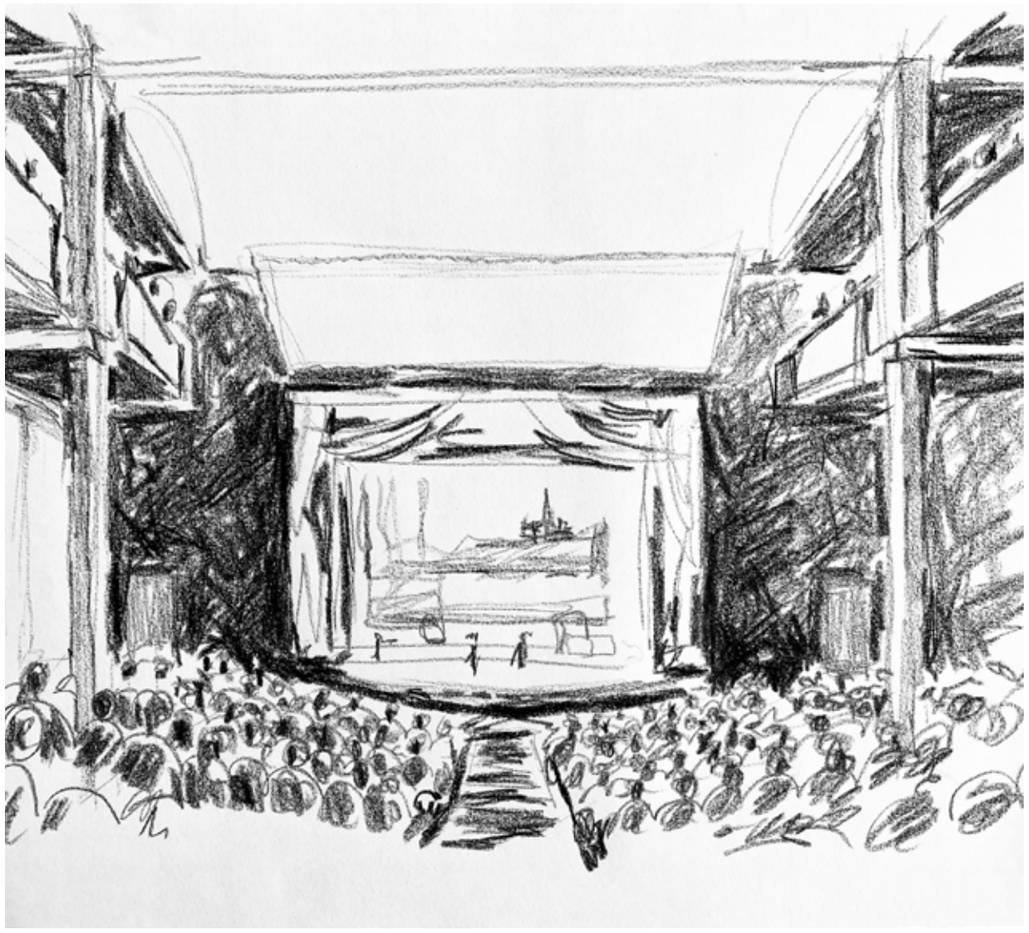

TRITA – ABE-MBT 2026:06

Stockholm, Sweden 2026.

www.kth.se

P3 KANDIDATARBETE
NILS WALDEMARSON
ÅK 3 STUDIO 2 VT26




NYA ELVERKET

I OCH MED ATT DRAMATEN BEHÖVDE STÄNGA SIN EXPERIMENTELLA TEATERSCEN ELVERKET INVID HISTORISKA MUSEET PÅ ÖSTERMALM PÅ GRUND AV HÖJDA HYROR SÅ STÄLLS MAN INFÖR FRÅGAN VAD KULTUREN EGENTLIGEN HAR FÖR PLATS I DAGENS STOCKHOLM? OM DET ÄR SÅ ATT DET PÅ GRUND AV BRISTANDE POLITISK VILJA EJ FINNS TILLRÄCKLIGA FINANSIELLA MEDEL FÖR KULTURELLA INSTITUTIONER ATT BEFINNA SIG INNANFÖR TULLARNA KANSKE DET ÄR SÅ ATT MAN BEHÖVER BLICKA UT MOT FÖRORTERNA FÖR POTENTIELLA NYA LOKALER? INFÖR KANDIDATARBETET VALDE JAG ATT UNDERSÖKA HUR EN NY TEATERBYGGNAD SKULLE KUNNA GESTALTAS I BREDÄNGS CENTRUM, VILKET VAR EN AV DE FÖRVALDA PLATSER VÅRA LÄRARE HADE VALT UT ÅT OSS. DET FINNS IDAG PÅ PLATSEN EN STOR PARKERINGSPLATS MEN OM MAN VALDE ATT PLACERA EN TEATER HÄR SKULLE DEN SPEGLA BREDÄNGS KYRKA PÅ ANDRA SIDAN CENTRUM OCH FULLÄNDA HARMONIN I DEN PLAN SOM UTGÖR BREDÄNGS CENTRUM. MITT PROGRAM BESTÅR DELS AV EN HUVUDBYGGNAD MED EN MER TRADITIONELL TEATERSCEN OCH EN LÄKTARE, DÄR LÄKTARENS LUTNING OCKSÅ FÖLJER LUTNINGEN PÅ EN BEFINTLIG GÅNGBANA INTILL. JAG HAR ÄVEN VALT ATT PLACERA EN MINDRE TEATERSCEN I EN SEPARAT BYGGNAD INTILL, DENNA SCEN SKULLE KUNNA HUSERA MINDRE FÖRESTÄLLNINGAR SOM DRAR MINDRE PUBLIK ELLER UPPSÄTTNINGAR SOM FÖREDRAR EN MER EXPERIMENTELL SCEN/BLACK BOX.



KARTLÄGGNING AV FASTA TEATRAR I SÖDERORT. RÖD PRICK: BREDÄNG.

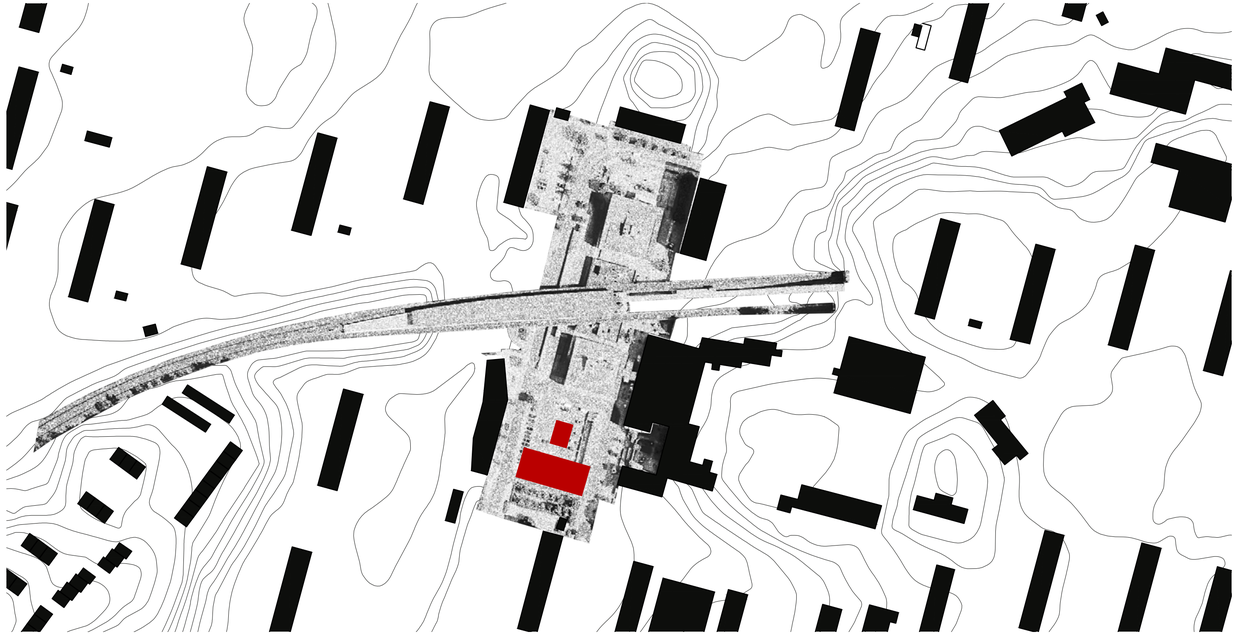

SITUATIONSPLAN

SKALA 1:2000

BREDÄNG PLATSBESÖK
FEB' 26



TUNNELBANEHUSET



INNE I BREDÄNGS KYRKA



VY ÖVER SÖDRA P-PLATSEN



P-PLATSEN SEDD FRÅN SÖDER



UTSTÄLLNING I EN AV GÅNGTUNLARNA



GÅNGTUNNEL FRÅN SÖDRA P-PLATSEN

BREDÄNG PLATSBESÖK
FEB' 26



VY ÖVER SÖDRA P-PLATSEN



SÖDER FRÅN T-BANAN



BREDÄNGS LIVS



GÅNGTUNNELN FRÅN SÖDRA P-PLATSEN





UTANFÖR BREDÄGNS KYRKA












SITUATIONSMODELL
MDF/PLYWOOD/ALTRÄ + SCHELLACK
SKALA 1:500

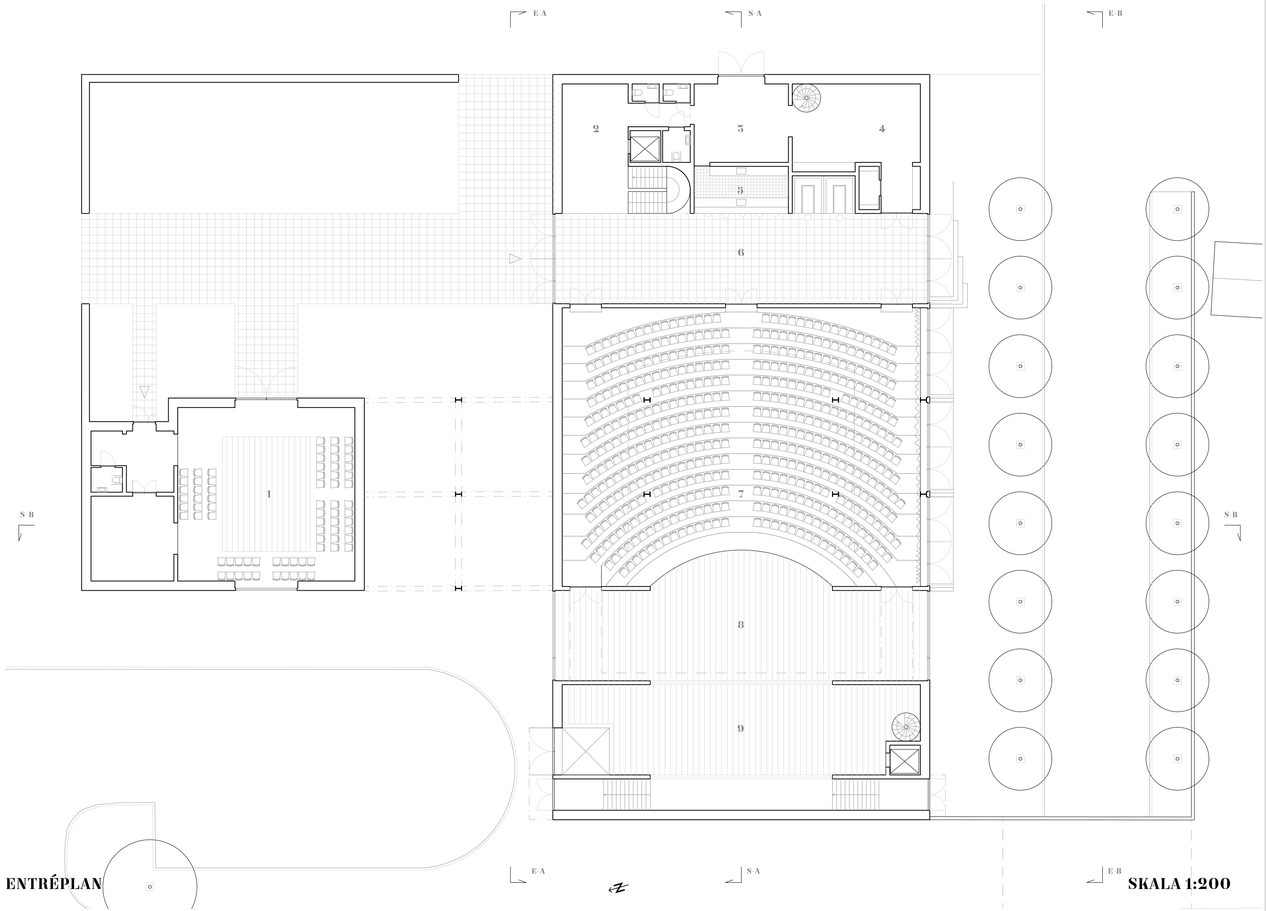

ENTRÉPLAN **SKALA 1:200**

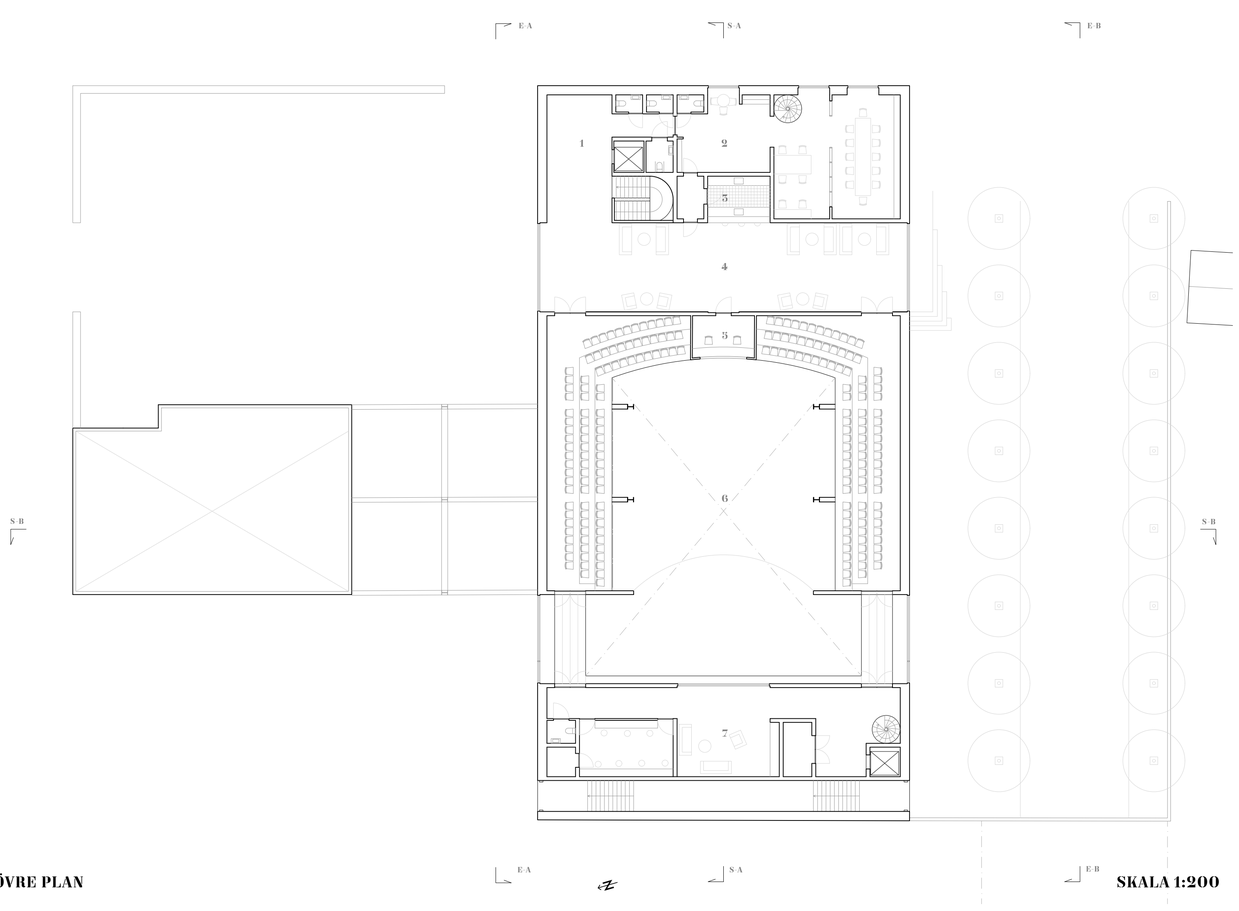


ÖVRE PLAN **SKALA 1:200**

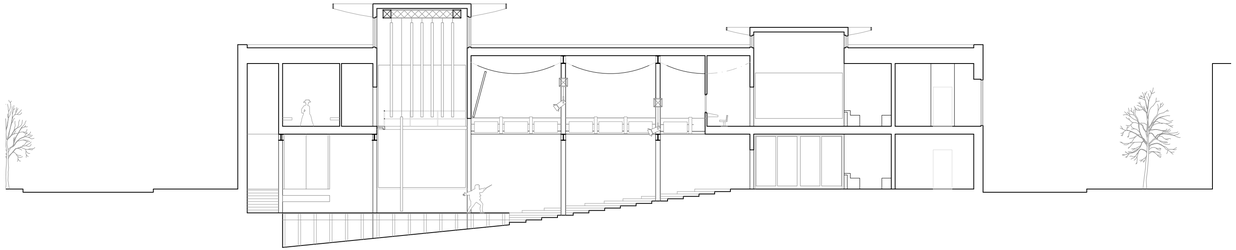

SEKTION A - A

SKALA 1:200

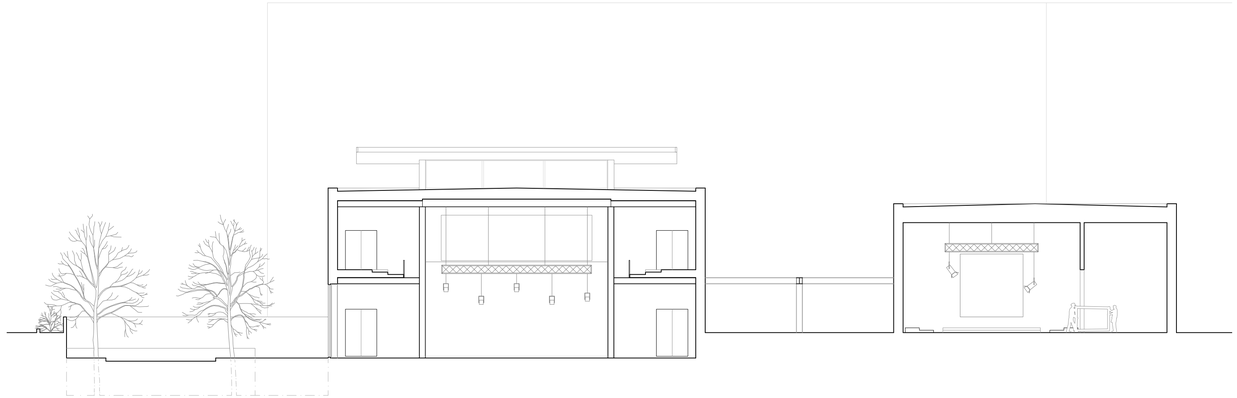


SEKTION B - B

SKALA 1:200



ELEVATION A - A

SKALA 1:200

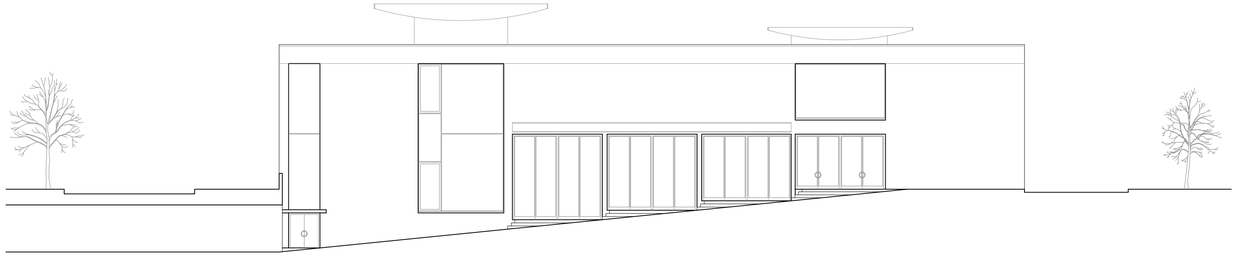

ELEVATION B - B

SKALA 1:200











MODELL
MDF/KARTONG + SCHELLACK
SKALA 1:200

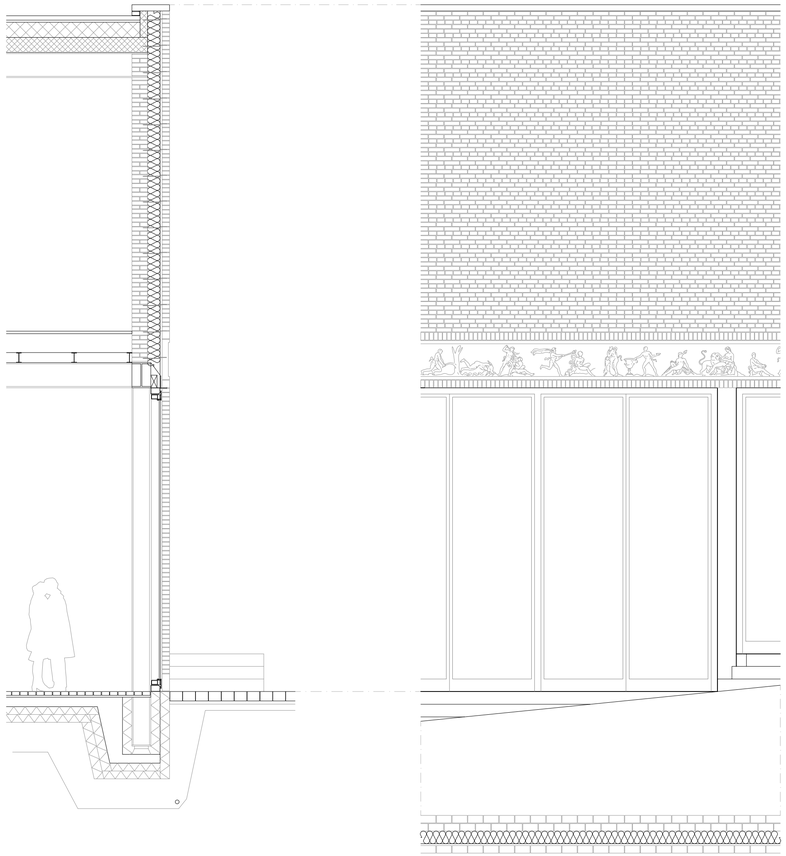

TEKNISKT SNITT

SKALA 1:50

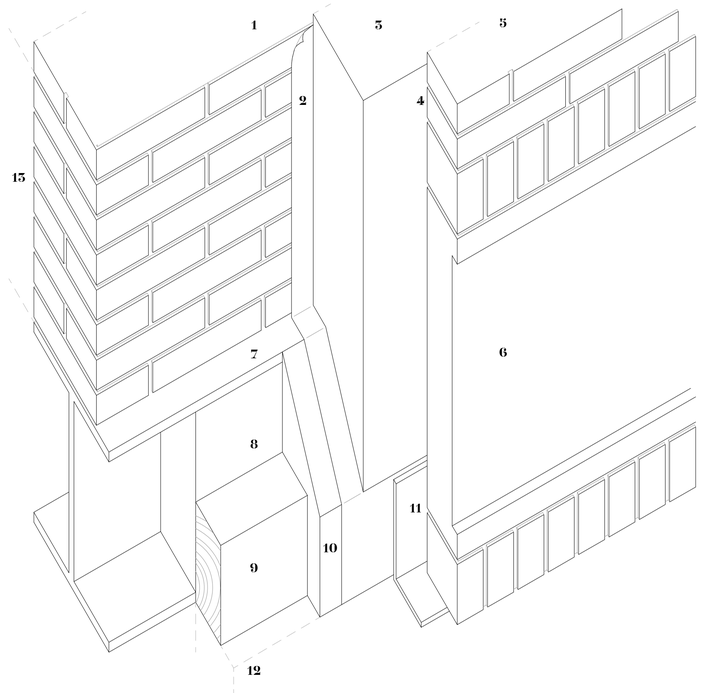


1. BÄRANDE INNERVÄGG TEGEL, 250 mm
2. FUKTSPÄRR
3. MJUK ISOLERING, 200 mm
4. LUFTSPALT, 30 mm
5. FASADTEGEL, 120 mm
6. FRIS, BETONG, 120 mm

7. BÄRANDE STÅLBALK, HEA400
8. IFYLLD BETONG, FÖR INFÄSTNING AV TRÄREGEL, 140 mm
9. TRÄREGEL, 100 mm
10. HÅRD ISOLERING, 50 mm
11. BÄRANDE STÅLPROFIL, FÄST I STÅLBALK

12. OVANSIDA STÅLPROFIL GLASPARTI

15. BJÄLKLAG MOT INNERVÄGG

TEKNISK DETALJ

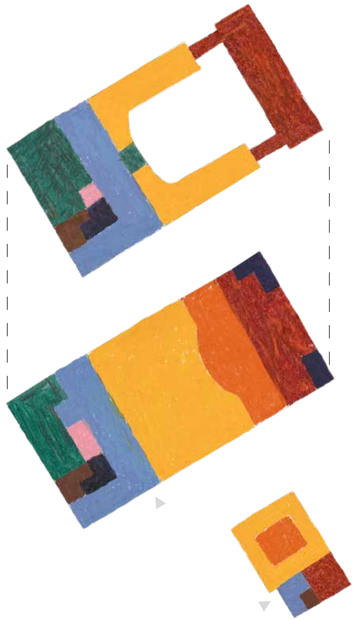

LÄKTARE

SCEN

BACKSTAGE


FOAJÉ

ADMIN/SERVANDE

KOMMUNIKATION


BAR/CAFÉ

WC

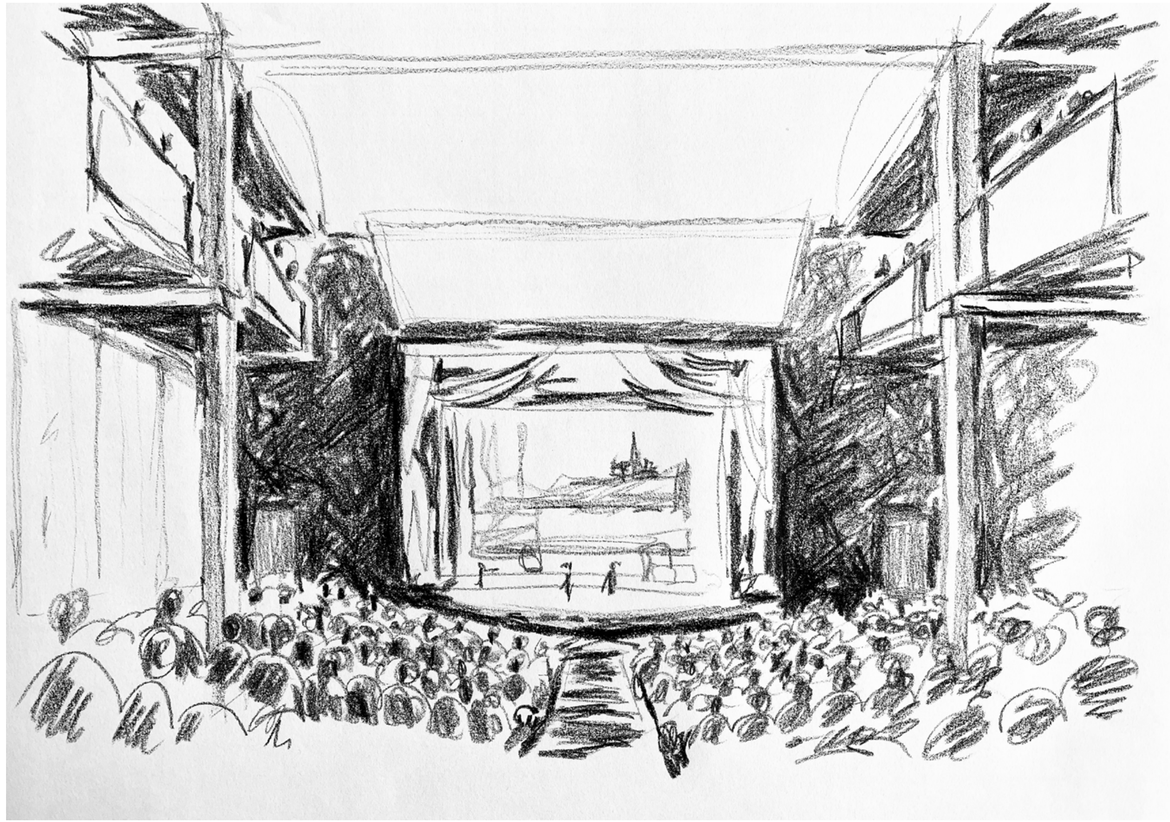






SCHEMATISK SPRÄNGAXO
AKRYL PÅ MDF

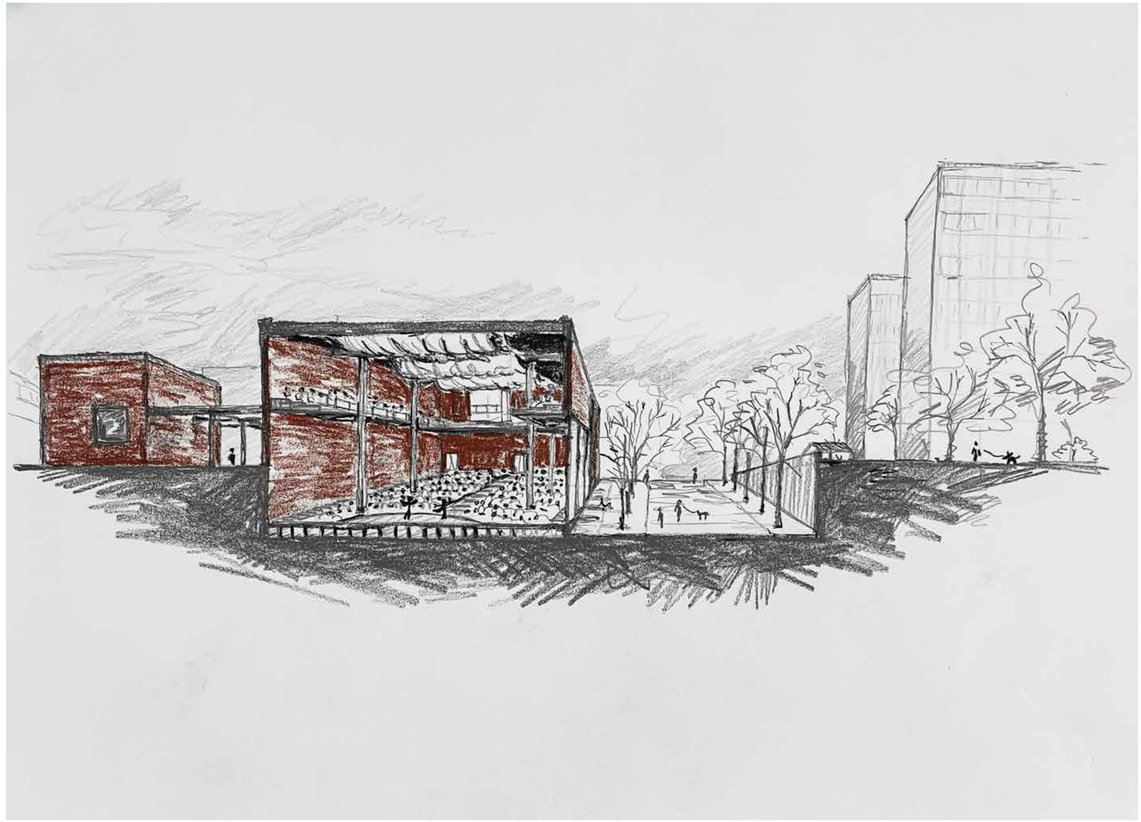


URVAL PROCESS

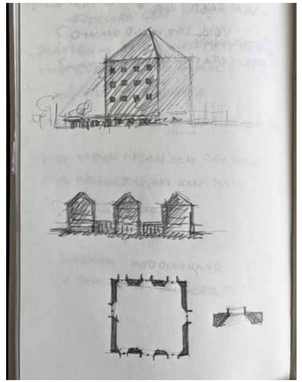

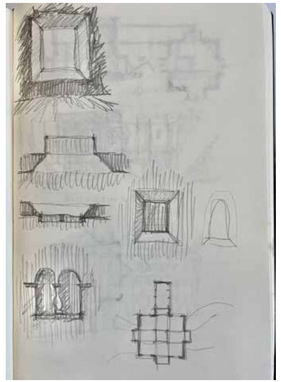

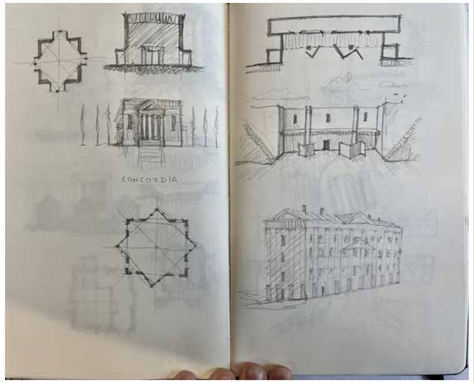




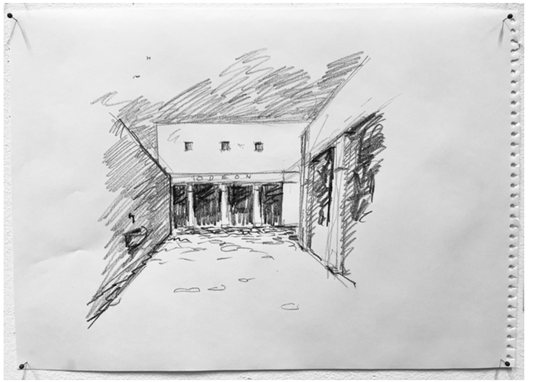

URVAL REFERENSER



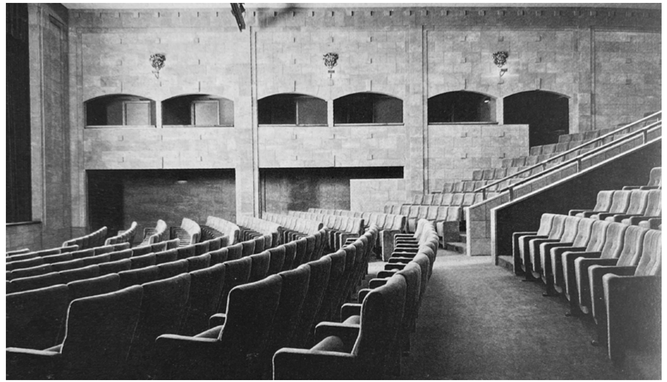

TEATRO DELLA COMPAGNIA,
ADOLFO NATALINI



ROMERSKA
TEATERBILJETTER



SAMMLUNG GOETZ,
HERZOG & DE MEURON

